


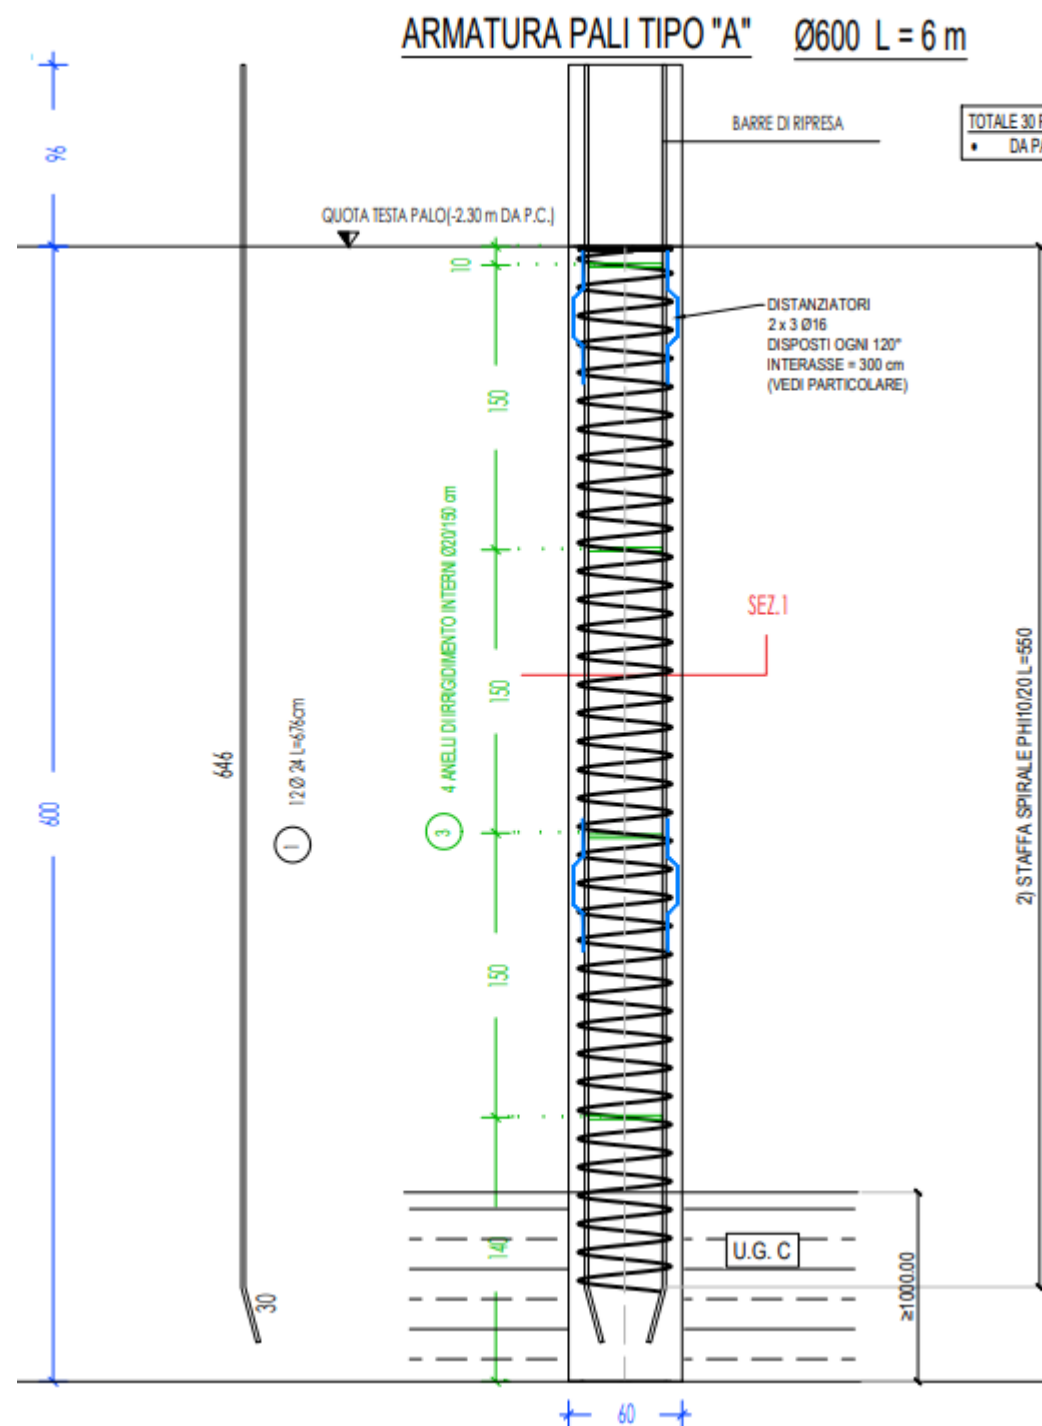

| COORDINATE PALI |            |             |              |     |
|-----------------|------------|-------------|--------------|-----|
| N.PALO          | Tipo       | X           | Y            | L   |
|                 |            | [m]         | [m]          | [m] |
| 14              | PAL TIPO A | 512396.5974 | 4349579.6571 | 6   |

**NOTA:**  
I COPRIFERRI SONO CALCOLATI TRA LA SUPERFICIE ESTERNA DELL'ELEMENTO E LA SUPERFICIE ESTERNA DELLA STAFFA O DEL FERRO ESTERNO.  
OVE NON ALTRIMENTI INDICATO LA SOVRAPPOSIZIONE MINIMA TRA LE BARRE SARA' PARI A 40 VOLTE IL DIAMETRO.

| TOLLERANZE ESECUTIVE                                                  |         |  |  |  |
|-----------------------------------------------------------------------|---------|--|--|--|
| □ Pali trivellati:                                                    |         |  |  |  |
| - coordinate planimetriche del centro del palo (rispetto al diametro) | ±5%     |  |  |  |
| - verticalità                                                         | ±1%     |  |  |  |
| - lunghezza                                                           | ± 25 cm |  |  |  |
| - diametro finito                                                     | ±5%     |  |  |  |
| - quota testa palo                                                    | ±5 cm   |  |  |  |

|  | TIPOLOGIA   | Ø PALO | L [m] | n. TOT | q.ta testapalo |
|--|-------------|--------|-------|--------|----------------|
|  | PALO TIPO A | Ø 600  | 6.00  | 30     | -2.30m         |

### Quote scavo a sezione per pali trivellati trasformatori

