


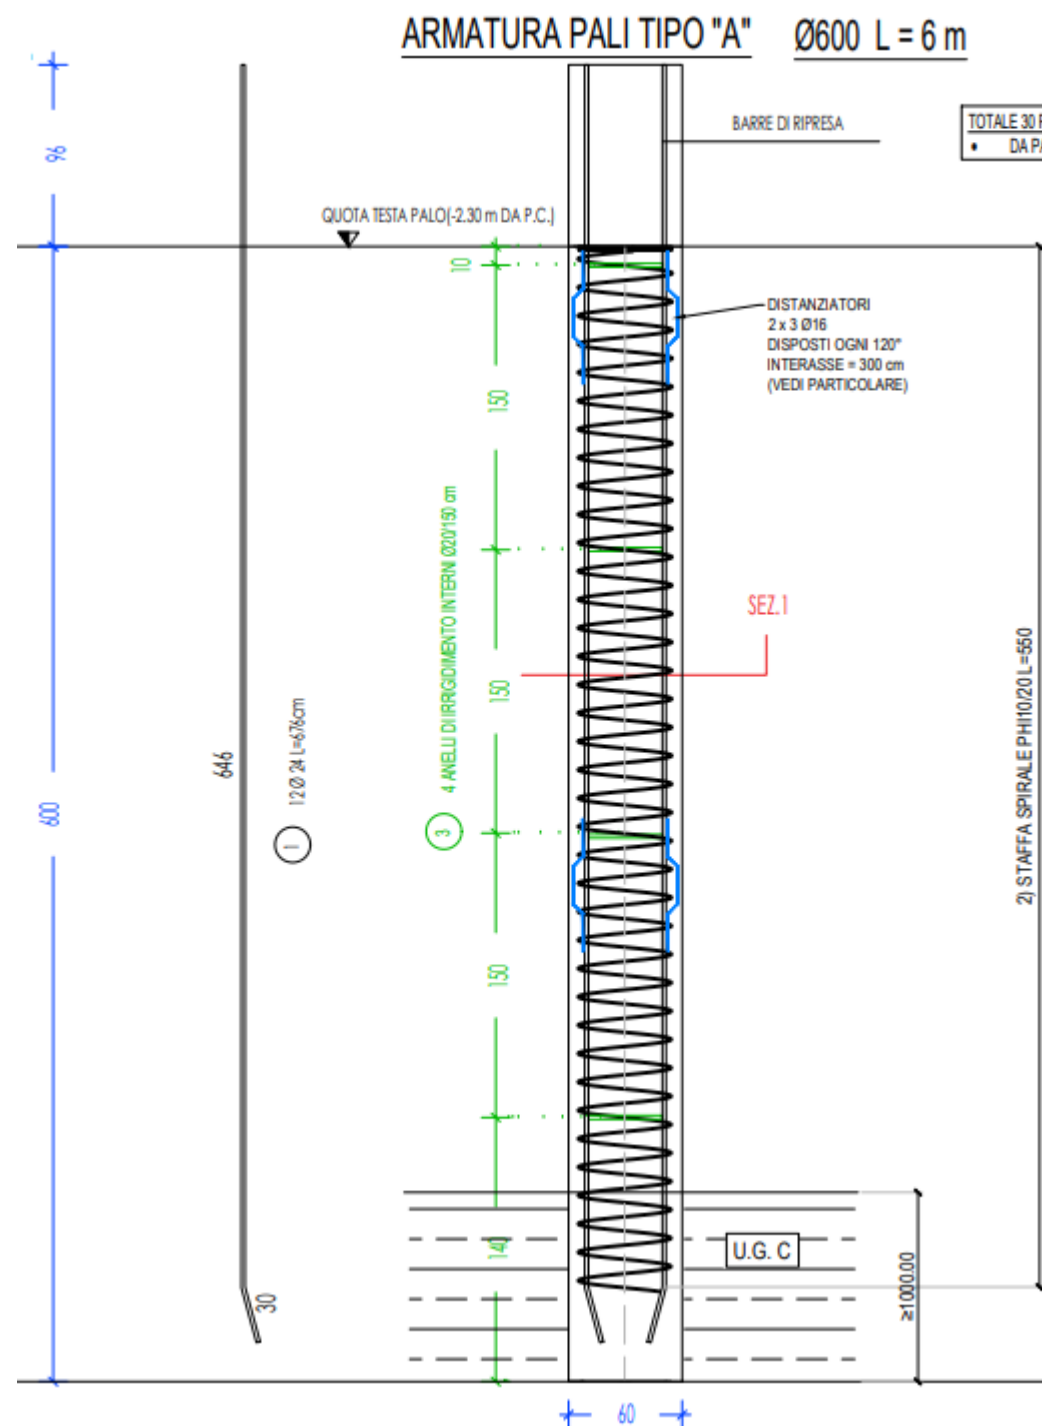

TUTALE 30 PALI:
• DA PALO N° 13 A PALO N° 42

COORDINATE PALI				
N°PALO	Tipo	X	Y	L
		[m]	[m]	[m]
16	PAL TIPO A	512403.5349	4349583.7162	6


NOTA:
I COPRIFERRI SONO CALCOLATI TRA LA SUPERFICIE ESTERNA DELL'ELEMENTO E LA SUPERFICIE ESTERNA DELLA STAFFA O DEL FERRO ESTERNO.
OVE NON ALTRIMENTI INDICATO LA SOVRAPPOSIZIONE MINIMA TRA LE BARRE SARA' PARI A 40 VOLTE IL DIAMETRO.

TOLLERANZE ESECUTIVE



- Pali trivellati:
- coordinate planimetriche del centro del palo (rispetto al diametro) ±5%
 - verticalità ±1%
 - lunghezza ± 25 cm
 - diametro finito ±5%
 - quota testa palo ±5 cm

	TIPOLOGIA	Ø PALO	L [m]	n. TOT	q.ta testapalo
	PALO TIPO A	Ø 600	6.00	30	-2.30m

Quote scavo a sezione per pali trivellati trasformatori

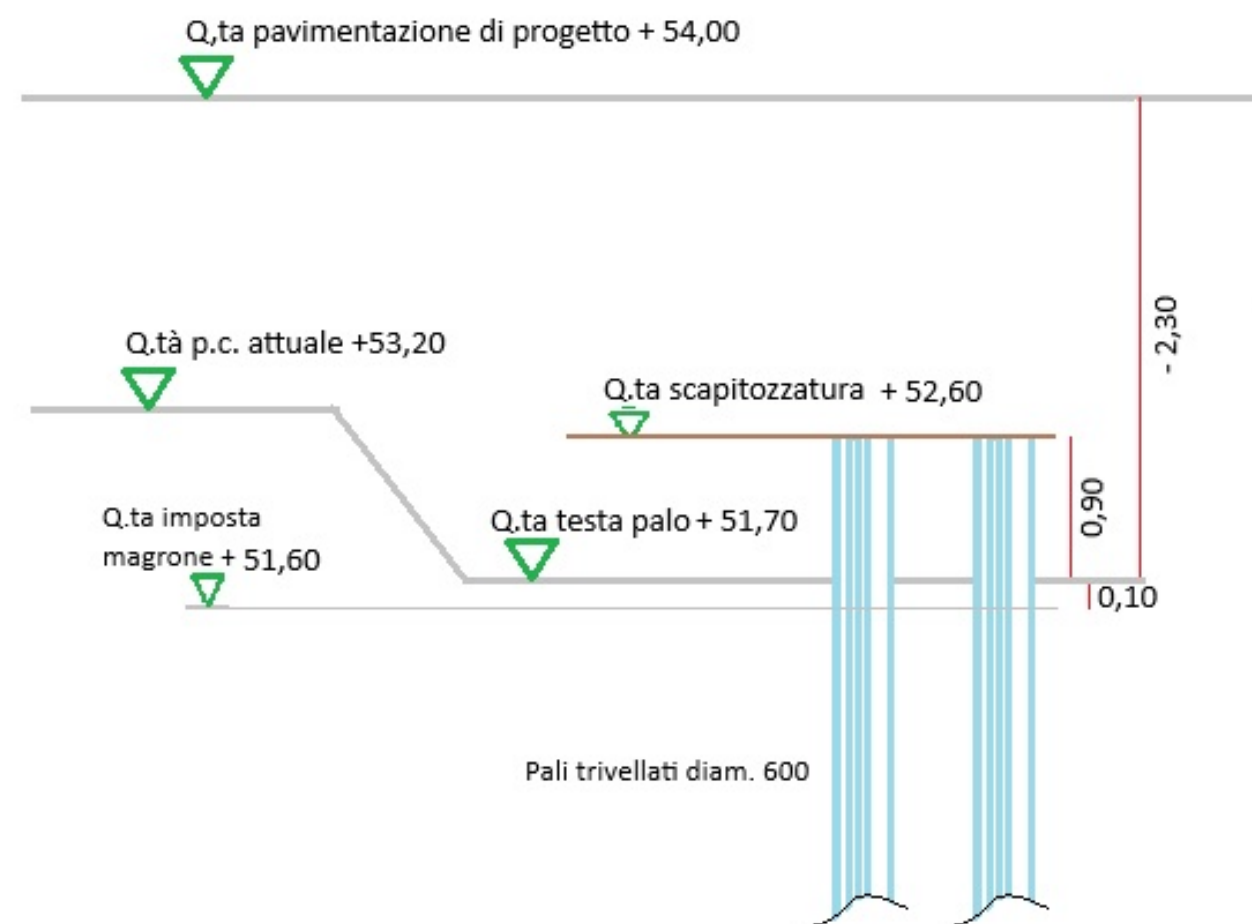

PARTICOLARE DISTANZIATORI

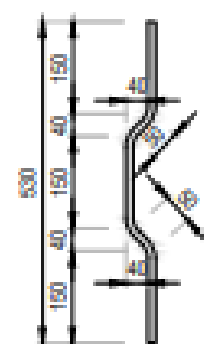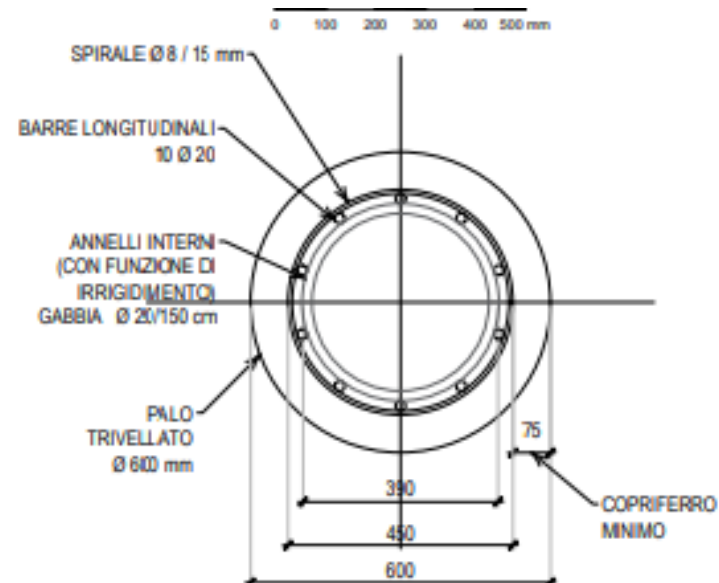

DISTANZIATORI
Ø 16 L= 55 cm