


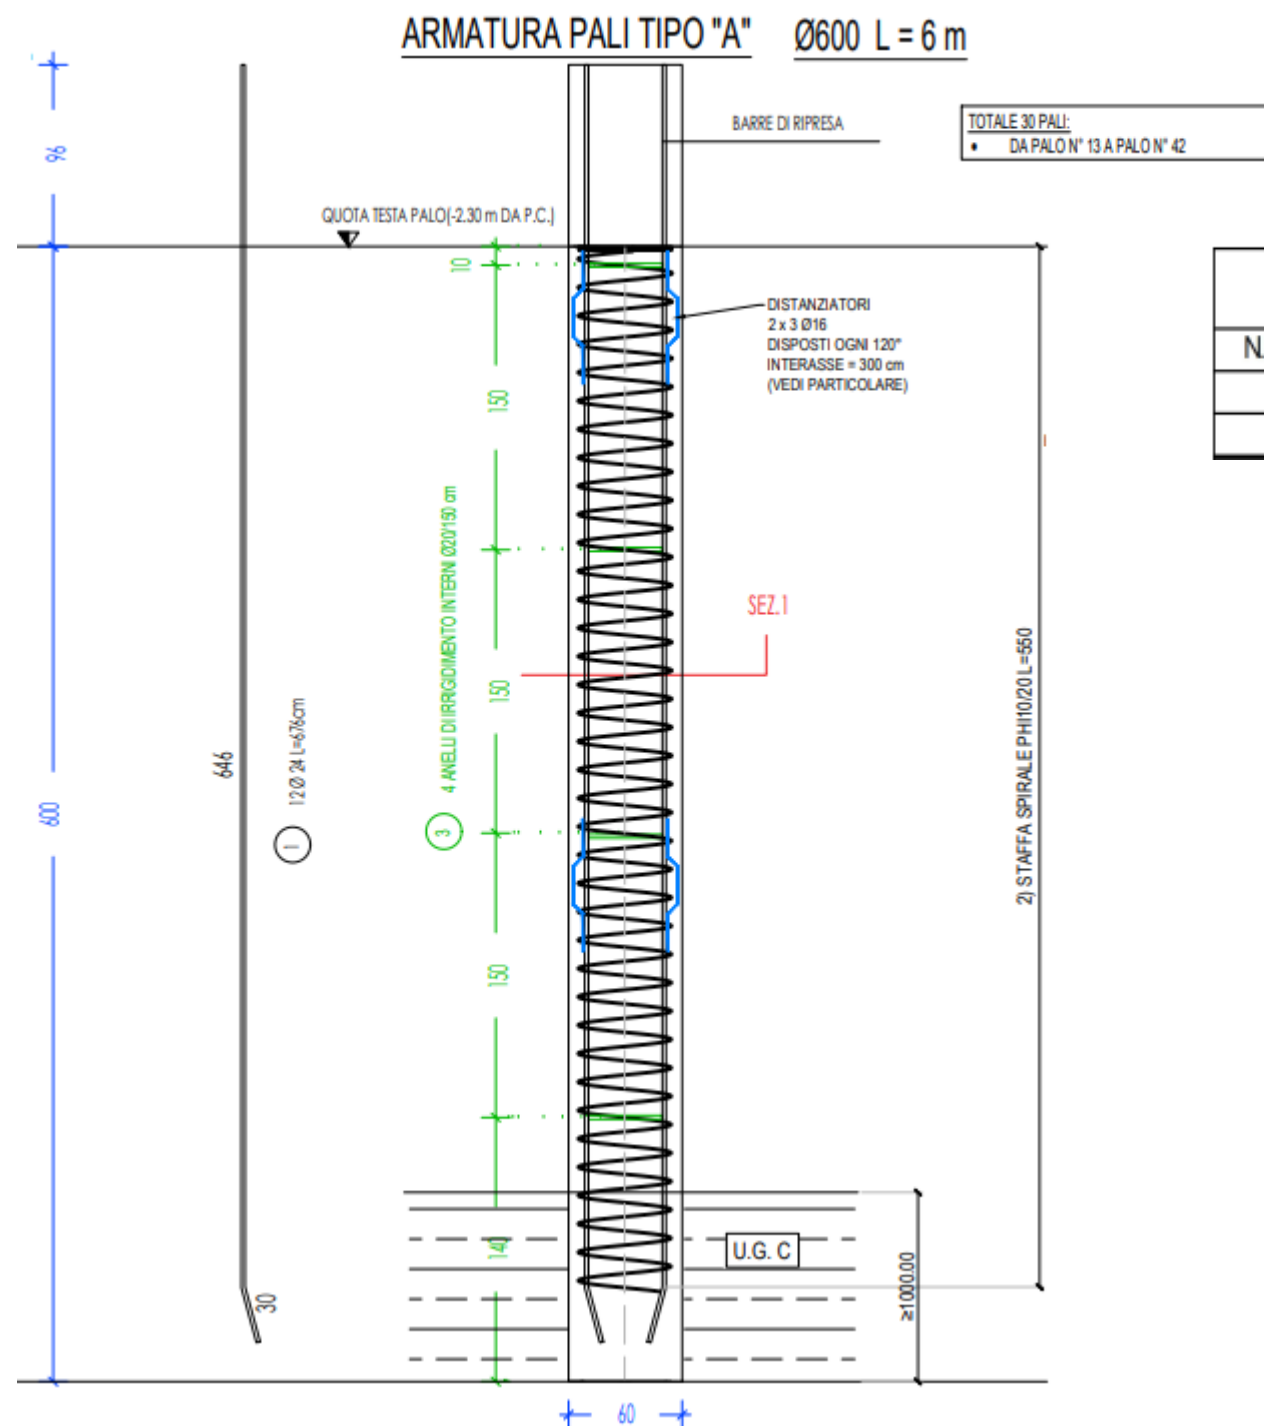


| COORDINATE PALI |      |     |     |     |
|-----------------|------|-----|-----|-----|
| N.PALO          | Tipo | X   | Y   | L   |
|                 |      | [m] | [m] | [m] |

**NOTA:**  
I COPRIFERRI SONO CALCOLATI TRA LA SUPERFICIE ESTERNA DELL'ELEMENTO E LA SUPERFICIE ESTERNA DELLA STAFFA O DEL FERRO ESTERNO.  
OVE NON ALTRIMENTI INDICATO LA SOVRAPPOSIZIONE MINIMA TRA LE BARRE SARA' PARI A 40 VOLTE IL DIAMETRO.

| TOLLERANZE ESECUTIVE                                                  |  |  |         |  |
|-----------------------------------------------------------------------|--|--|---------|--|
| □ Pali trivellati:                                                    |  |  |         |  |
| - coordinate planimetriche del centro del palo (rispetto al diametro) |  |  | ±5%     |  |
| - verticalità                                                         |  |  | ±1%     |  |
| - lunghezza                                                           |  |  | ± 25 cm |  |
| - diametro finito                                                     |  |  | ±5%     |  |
| - quota testa palo                                                    |  |  | ±5 cm   |  |

|  | TIPOLOGIA   | Ø PALO | L [m] | n. TOT | q.ta testapalo |
|--|-------------|--------|-------|--------|----------------|
|  | PALO TIPO A | Ø 600  | 6.00  | 30     | -2.30m         |

### Quote scavo a sezione per pali trivellati trasformatori

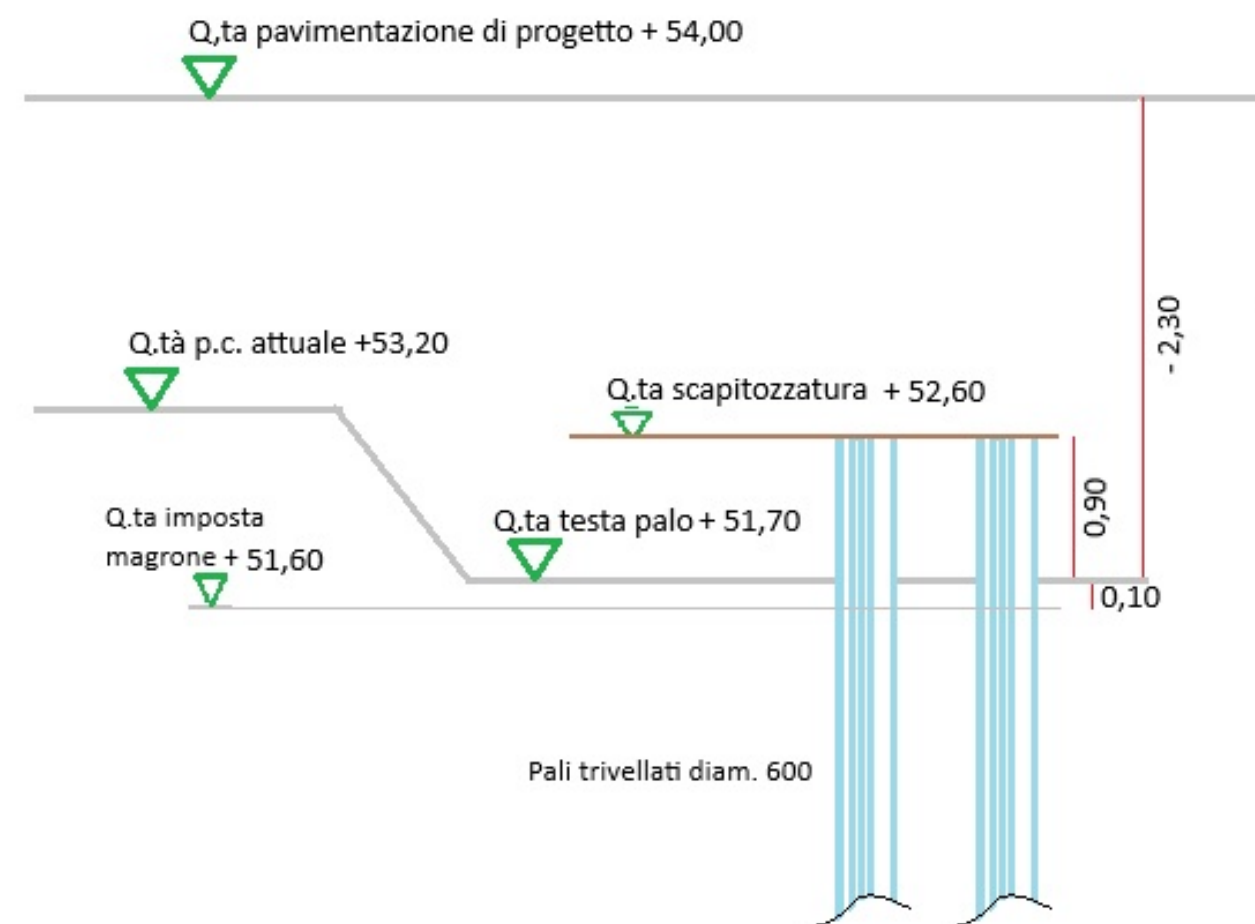

### PARTICOLARE DISTANZIATORI

