


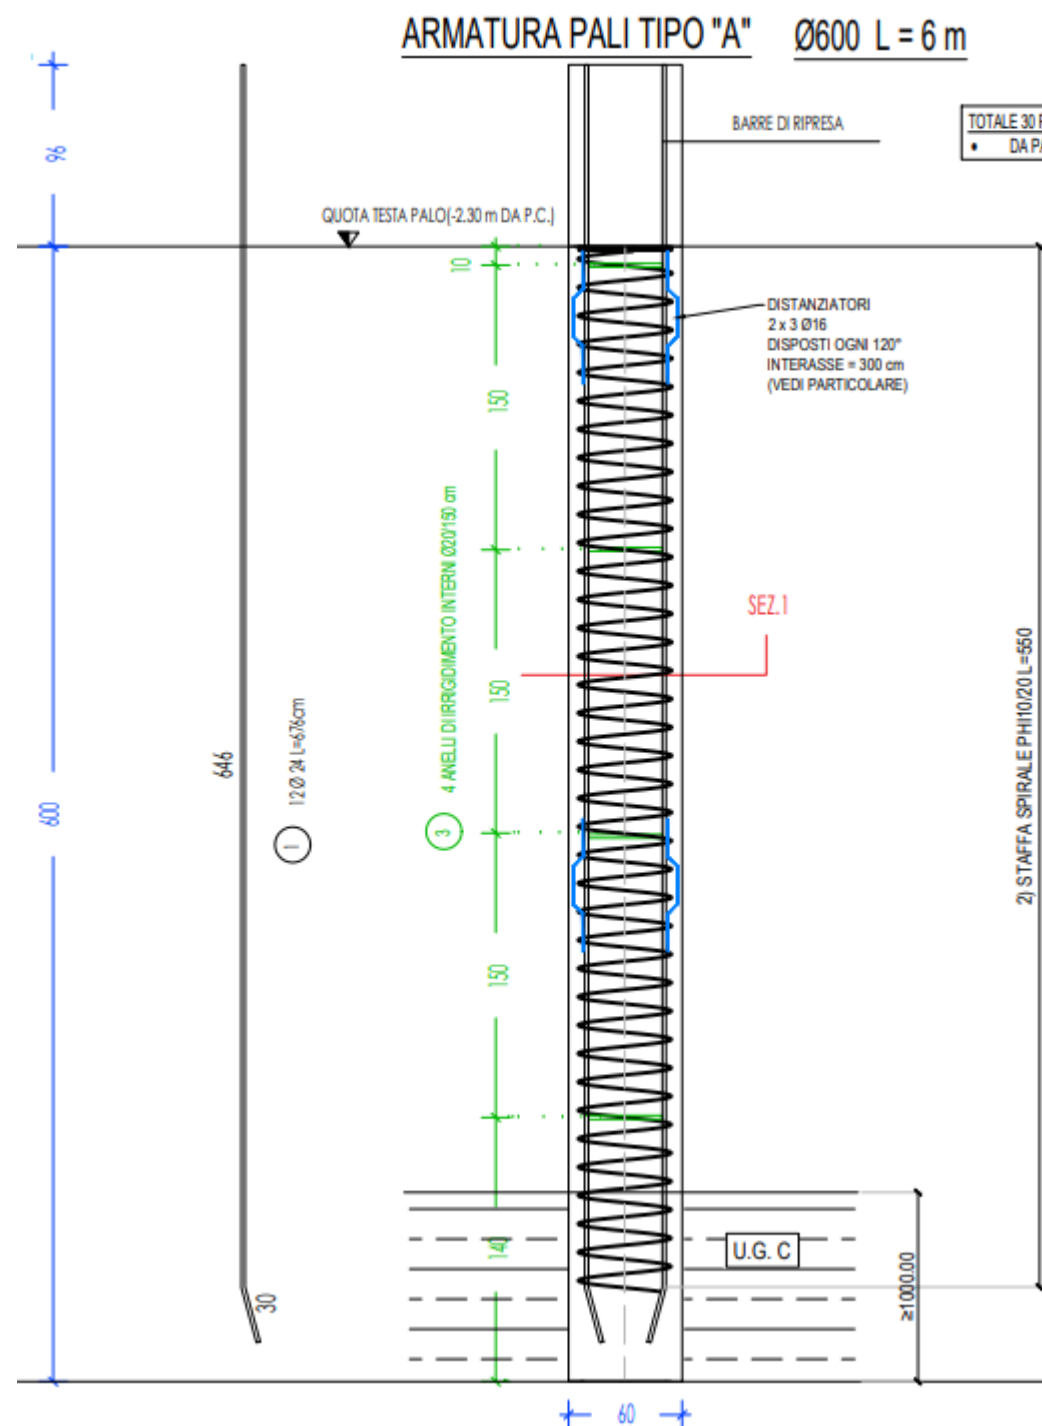



COORDINATE PALI				
N.PALO	Tipo	X	Y	L
		[m]	[m]	[m]

NOTA:
I COPRIFERRI SONO CALCOLATI TRA LA SUPERFICIE ESTERNA DELL'ELEMENTO E LA SUPERFICIE ESTERNA DELLA STAFFA O DEL FERRO ESTERNO.
OVE NON ALTRIMENTI INDICATO LA SOVRAPPOSIZIONE MINIMA TRA LE BARRE SARA' PARI A 40 VOLTE IL DIAMETRO.


TOLLERANZE ESECUTIVE				
□ Pali trivellati:				
- coordinate planimetriche del centro del palo (rispetto al diametro)				±5%
- verticalità				±1%
- lunghezza				± 25 cm
- diametro finito				±5%
- quota testa palo				±5 cm

	TIPOLOGIA	Ø PALO	L [m]	n. TOT	q.ta testapalo
	PALO TIPO A	Ø 600	6.00	30	-2.30m

Quote scavo a sezione per pali trivellati trasformatori

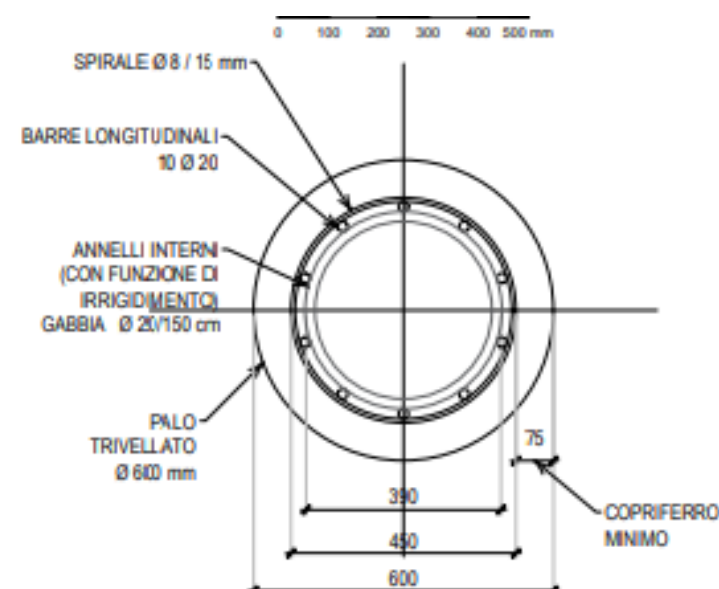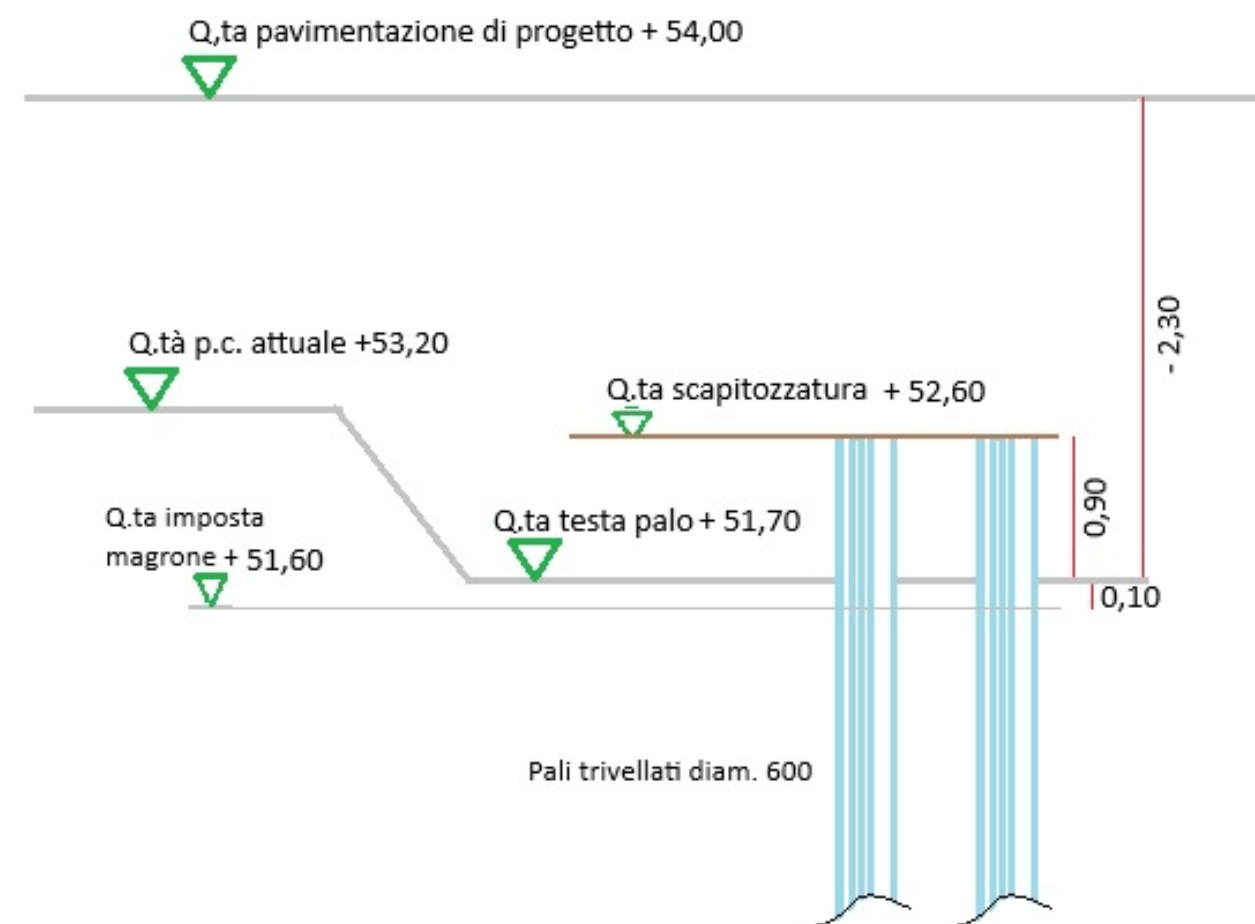

PARTICOLARE DISTANZIATORI

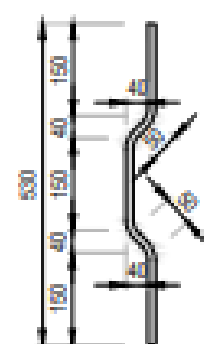

DISTANZIATORI
Ø 16 L= 55cm