


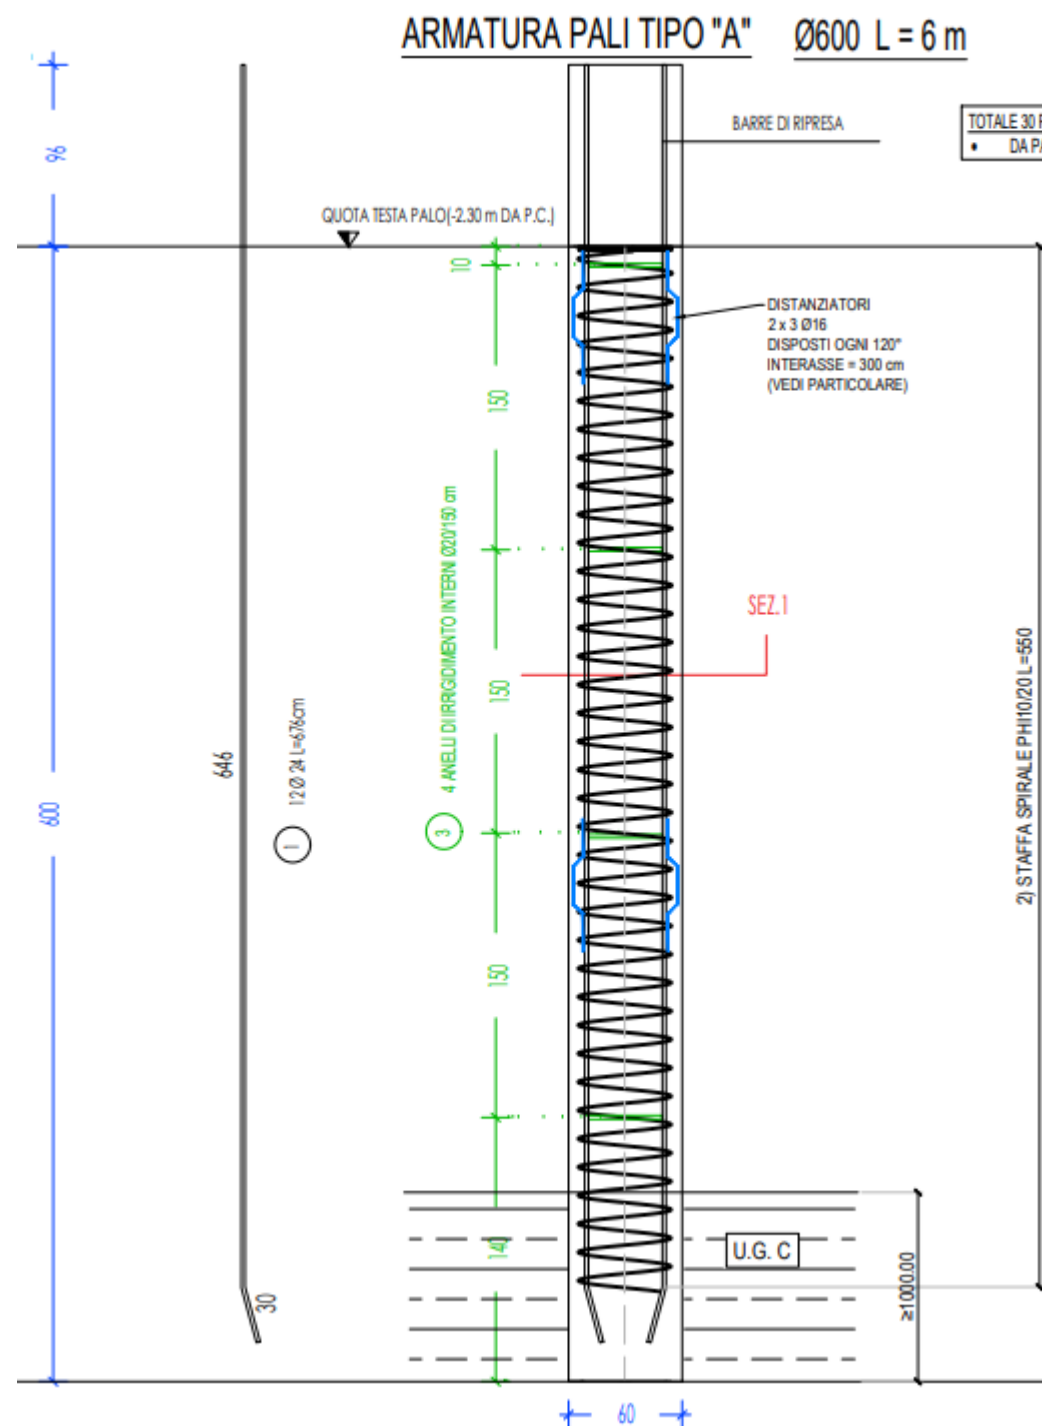

TOTALE 30 PALI:
• DA PALO N° 13 A PALO N° 42


COORDINATE PALI				
N.PALO	Tipo	X	Y	L
		[m]	[m]	[m]

NOTA:
I COPRIFERRI SONO CALCOLATI TRA LA SUPERFICIE ESTERNA DELL'ELEMENTO E LA SUPERFICIE ESTERNA DELLA STAFFA O DEL FERRO ESTERNO.
OVE NON ALTRIMENTI INDICATO LA SOVRAPPOSIZIONE MINIMA TRA LE BARRE SARA' PARI A 40 VOLTE IL DIAMETRO.




TOLLERANZE ESECUTIVE				
□ Pali trivellati:				
- coordinate planimetriche del centro del palo (rispetto al diametro)			±5%	
- verticalità			±1%	
- lunghezza			± 25 cm	
- diametro finito			±5%	
- quota testa palo			±5 cm	

	TIPOLOGIA	Ø PALO	L [m]	n. TOT	q.ta testapalo
	PALO TIPO A	Ø 600	6.00	30	-2.30m

Quote scavo a sezione per pali trivellati trasformatori

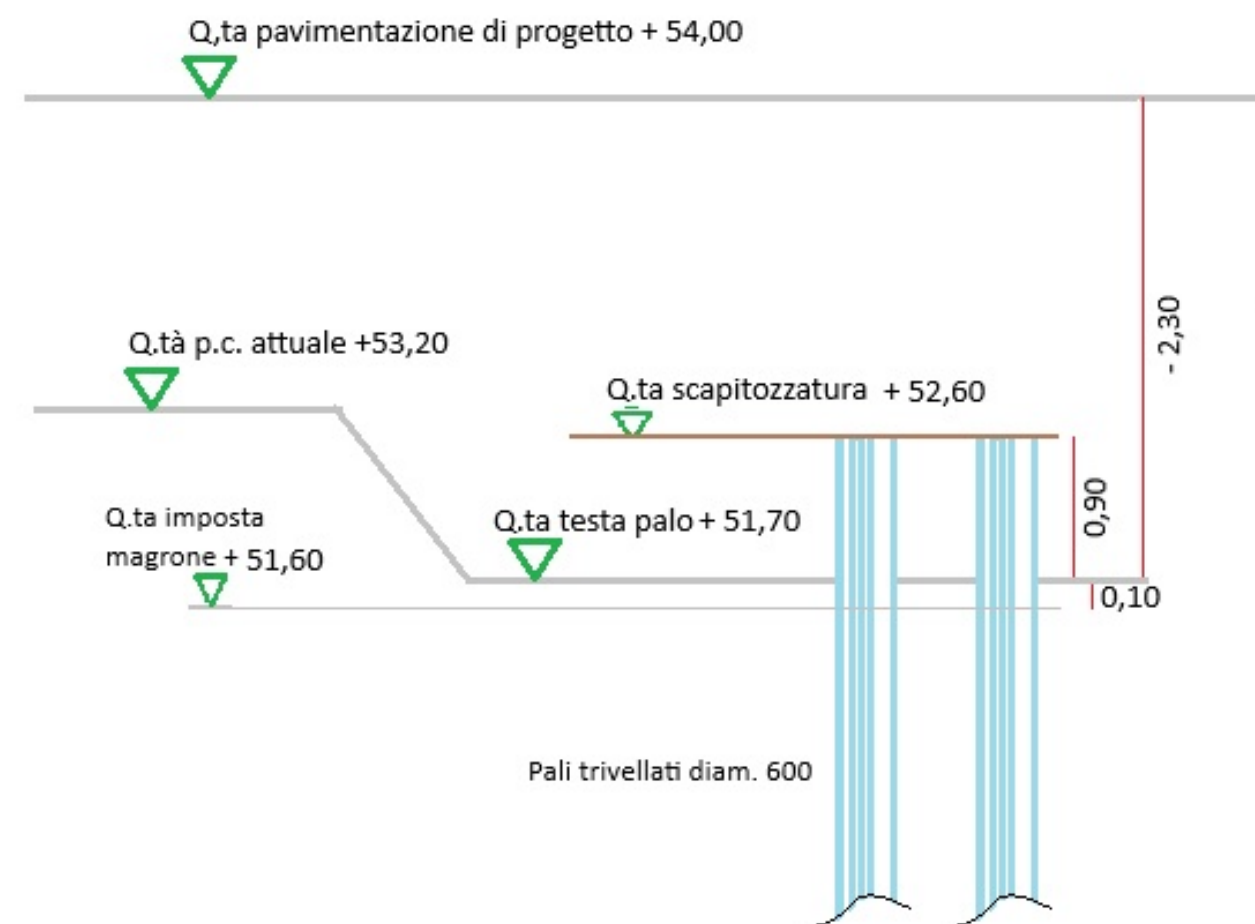

PARTICOLARE DISTANZIATORI

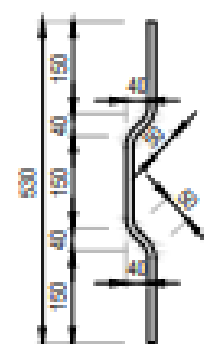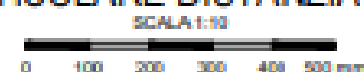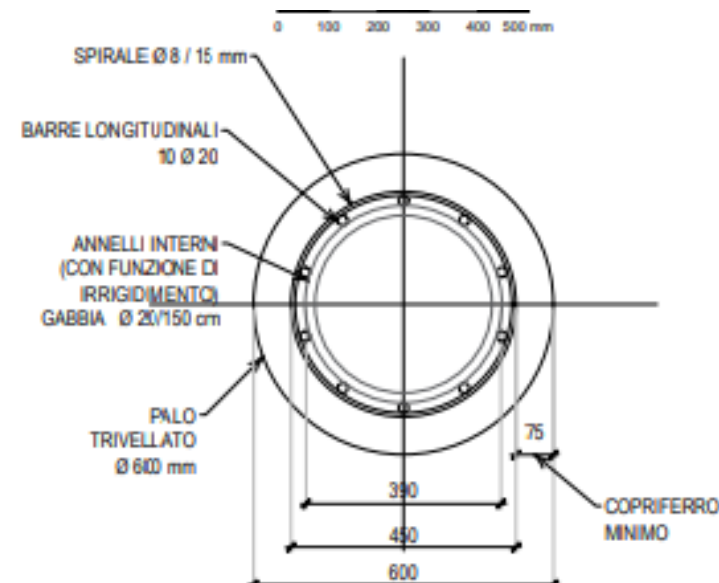

DISTANZIATORI
Ø 16 L= 55cm